

Удмуртская Республика
г. Ижевск
Бюджетное учреждение Удмуртской Республики
“Центр кадастровой оценки и технической инвентаризации
недвижимого имущества”

Район Октябрьский

ТЕХНИЧЕСКИЙ ПАСПОРТ
нежилого помещения


по адресу: Удмуртская Республика, г. Ижевск, ул. Холмогорова, 17
Литера «Г», мансарда

Инвентарный номер	35027
-------------------	-------

Паспорт составлен по состоянию на “ 18 ” февраля 2021 г.

Ситуационный план


"Мансарда" ЛИТЕРА "Г"

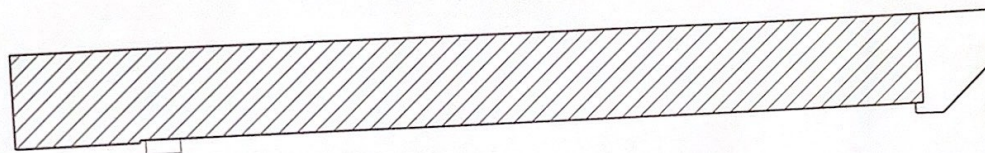

БУ УР "ЦКО БТИ" г. Ижевск				
Ситуационный план				
Инженер	ФИО Домашних А.А. <i>А.А. Домашних</i>	Дата 25.02.2021 г.	Адрес объекта: Удмуртская Республика, г. Ижевск, ул. Холмогорова, 17	Лист 2 Листов 5 Масштаб 1:500

Постажный план

"Мансарда" ЛИТЕРА "Г"

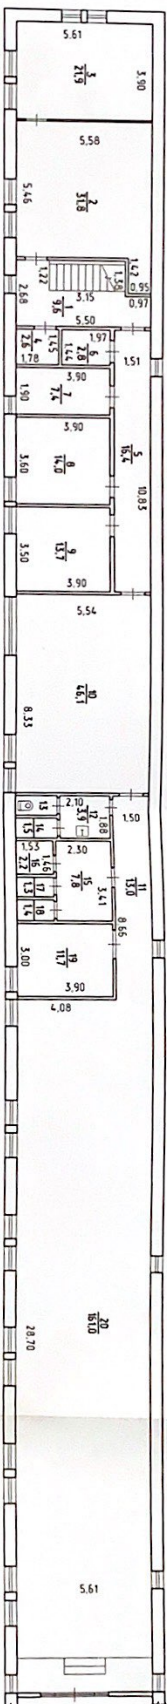

БУ УР "ЦКО БТИ" г. Ижевск			
Поступающий план			
Инженер	ФИО	Дата	Адрес объекта:
	Домашних А.А.	25.02.2021 г.	Удмуртская Республика, г. Ижевск, ул. Холмогорода, 17
			Лист 3 Листов 5 Масштаб 1:200

№ 17

Этаж и номер квартиры по плану	Номер помещения (ком. инт., подкомнат., кухня, ванна, коридор и т.п.)	Назначение помещений, жилого помещения, капитальное, нежилого, складского и т.п.	Площадь по внутреннему обмеру в квадратных метрах, в т.ч., предназначенная под помещения																							Высота помещений по внутреннему обмеру
			Жилая						Промышленные (производственные)		Складские		Предприятия бытового обслуживания		Канцелярские		Предприятия общественного питания		Прочие		Места общественного пользования					
			Площадь квартир	Жилая площадь квартир	Подсобная	Лоджии, балконы, террасы, веранды, кладовые с коффе	Основная	Подсобная	Основная	Подсобная	Основная	Подсобная	Основная	Подсобная	Основная	Подсобная	Основная	Подсобная	Основная	Подсобная						
1	2	3	4	5	6	8	9	10	11	12	13	14	15	16	17	18	19	20	21	22	23	24	25	26	27	28
Г	мансарда	1		лестничная клетка	9,6																					
2021 г		2		кабинет	31,8																					
		3		кабинет	21,9																31,8					
		4		санузел	2,6																21,9					
		5		коридор	16,4																	2,6				
		6		подсобное	2,8																	16,4				
		7		кабинет	7,4																	2,8				
		8		кабинет	14,0																7,4					
		9		кабинет	13,7																14,0					
		10		обслуживающий зал	46,1																13,7					
		11		коридор	13,0																46,1					
		12		санузел	3,9																	13,0				
		13		санузел	1,5																3,9					
		14		санузел	1,5																	1,5				
		15		санузел	7,8																	1,5				
		16		санузел	2,2																	7,8				
		17		санузел	1,3																	2,2				
		18		санузел	1,4																	1,3				
		19		техническое помещение	11,7																	1,4				
		20		обслуживающий зал	161,0																	11,7				
				Итого мансарды:	371,6																	161,0				
																						307,6				
																						64,0				

Перечень документов, прилагаемых к техническому паспорту

№№ п.п.	Наименование документа	Масштаб	Количество листов	Примечание

Исполнил



/Домашних А.А. / « 25 » 02 2021 г.

Директор

начальник отдела
кастровых работ
Андреев О.В.

/Возмищева Н.А./ « 25 » 02 2021 г.

Прошито,
прошнуровано
скреплено печатью

Для на 5 листах

25.08.2021

